
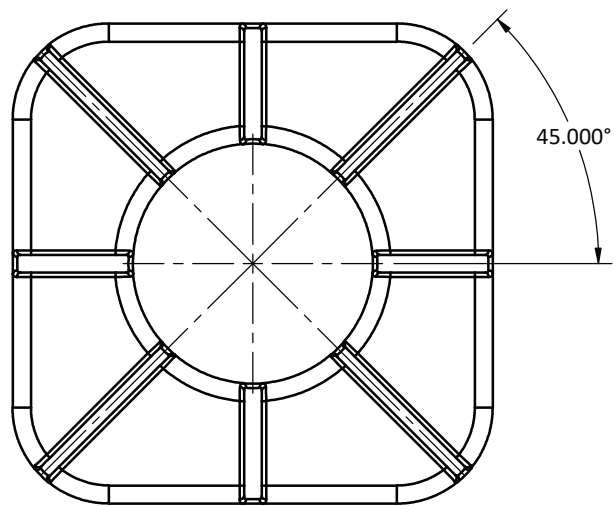
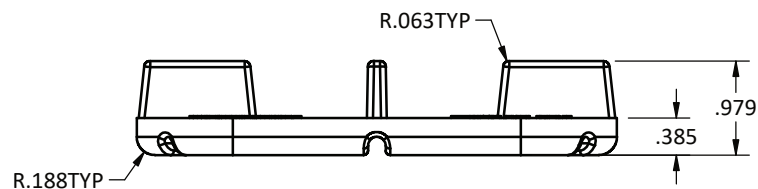


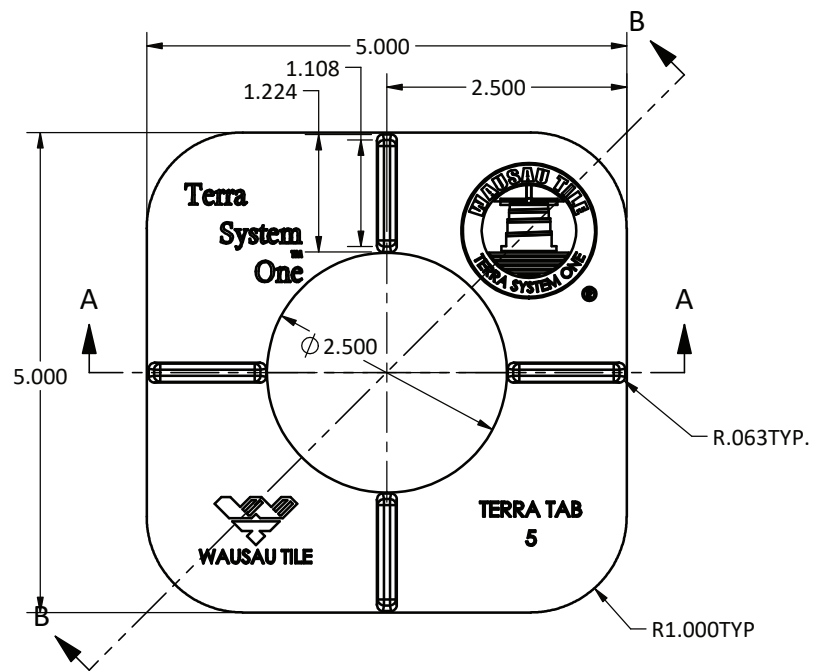


1. Linear Dimensions

Nominal Length (mm)	Nominal Length (in)	Tolerance (mm)	Tolerance (in)
0.5 – 3	0.020 – 0.118	±0.20	±0.008
>3 – 6	0.118 – 0.236	±0.30	±0.012
>6 – 30	0.236 – 1.181	±0.50	±0.020
>30 – 120	1.181 – 4.724	±0.80	±0.031
>120 – 400	4.724 – 15.748	±1.20	±0.047

2. Angular Dimensions


Shorter Side Length (mm)	Shorter Side Length (in)	Coarse (c) Tolerance
≤10	≤0.394	±1°30' (±1.5°)
>10 – 50	0.394 – 1.969	±1°
>50 – 120	1.969 – 4.724	±0°30' (±0.5°)

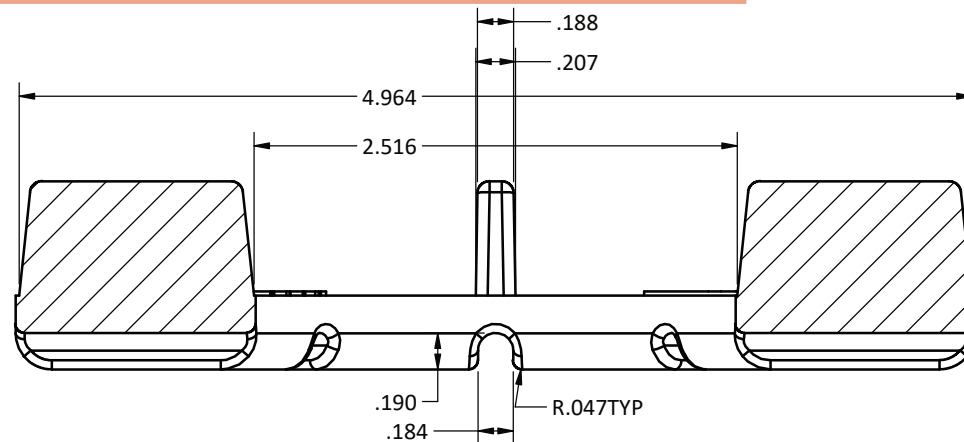

SECTION A-A
SCALE 1 : 1

3. External Radii and Chamfers

Nominal Radius / Chamfer (mm)	Nominal Radius / Chamfer (in)	Tolerance (mm)	Tolerance (in)
0.5 – 3	0.020 – 0.118	±0.20	±0.008
>3 – 6	0.118 – 0.236	±0.50	±0.020
>6 – 30	0.236 – 1.181	±1.00	±0.039
>30	>1.181	±2.00	±0.079

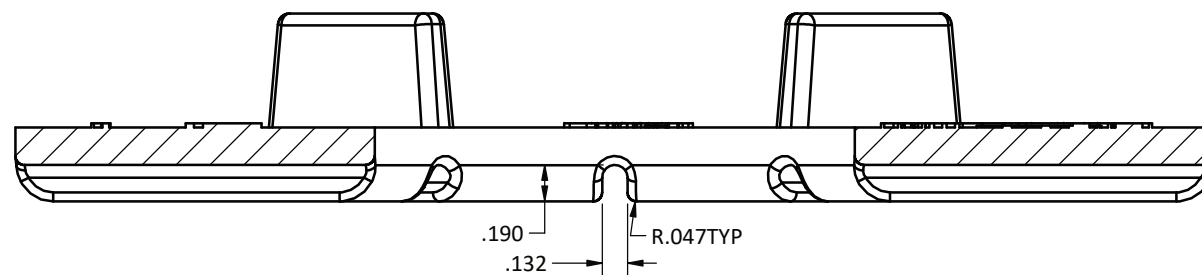

SECTION B-B
SCALE 1 : 1

NOTES:

- PRE-FORMED WEIGHT 180 GRAMS
- FINISHED WEIGHT 145 GRAMS
- MATERIAL: SBR RUBBER
- 70 DUROMETER



WAUSAU TILE

P.O. BOX 1520, WAUSAU, WI 54402-1520

800-388-8728

E-MAIL: WTILE@WAUSAUTILE.COM

WEBSITE: WWW.WAUSAUTILE.COM

REVISIONS

	NAME	DATE	NOTES
1	MWJ	6/15/11	REDRAWN COM
2	MWJ	3/13/12	CHNGE DIMS
3	MWJ	3/14/12	REV. SHAPE
4	JEM	10/15/15	REDRAWN IN SW
5	BMB	10/09/25	REVISED TEXT
6			
7			
8			

CONFIDENTIAL INFORMATION

THESE DRAWINGS, SPECIFICATIONS AND OTHER INFORMATION AND DOCUMENTS ACCOMPANYING THEM ARE THE CONFIDENTIAL AND PROPRIETARY PROPERTY OF WAUSAU TILE, INC. THE DRAWINGS THEMSELVES SHALL BELONG TO THE OWNER FOR USE ONLY ON THE PROJECT. ANY ADDITIONAL USE SHALL REQUIRE THE PRIOR WRITTEN APPROVAL OF WAUSAU TILE, INC. THE PROPRIETARY INFORMATION CONTAINED WITHIN THE DRAWINGS AND THE DOCUMENTS IS AND SHALL REMAIN THE SOLE PROPERTY OF WAUSAU TILE, INC.

#5 TERRA TAB 3/16" JOINT

UNLESS OTHERWISE SPECIFIED
DIMENSIONS ARE IN INCHES
TOLERANCE:
FRACTIONS ± 1/8" ANGLE ±0.5°
DIM: 2-PL ±0.01 3-PL ±0.05

DRAWN BY: GRM 12/23/1986

DATE: 10/9/2025

MATERIAL:

CO NUMBER:

WEIGHT:

NUMBER: 10001 - REV.1